

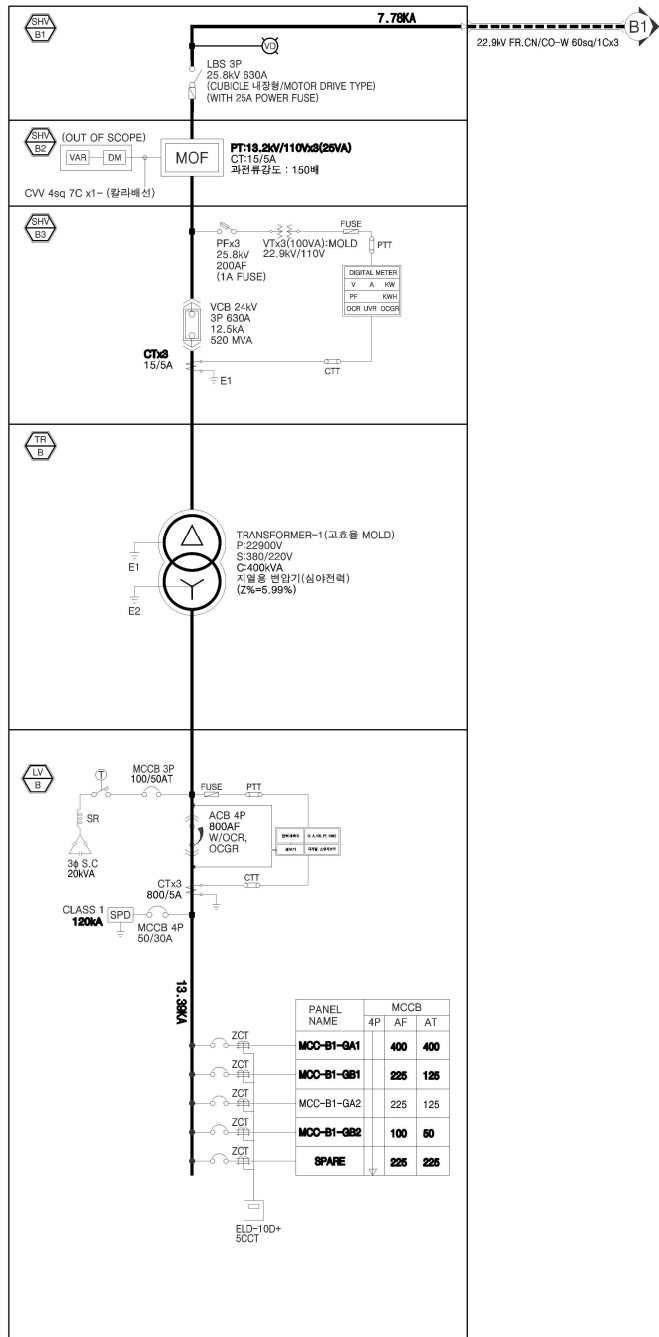


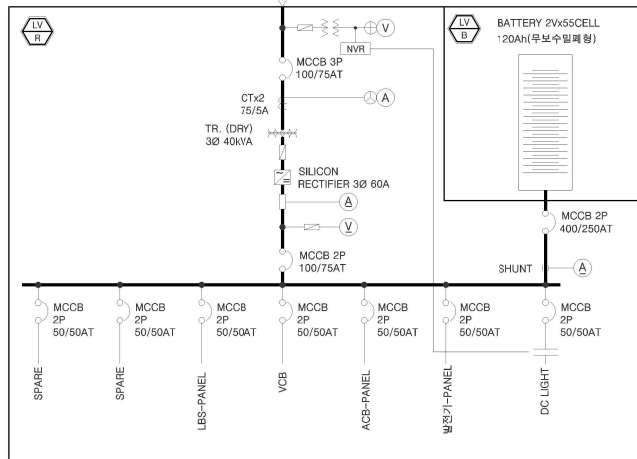

수변전설비 단선 결선도-1

A1: NONE, A3: NONE

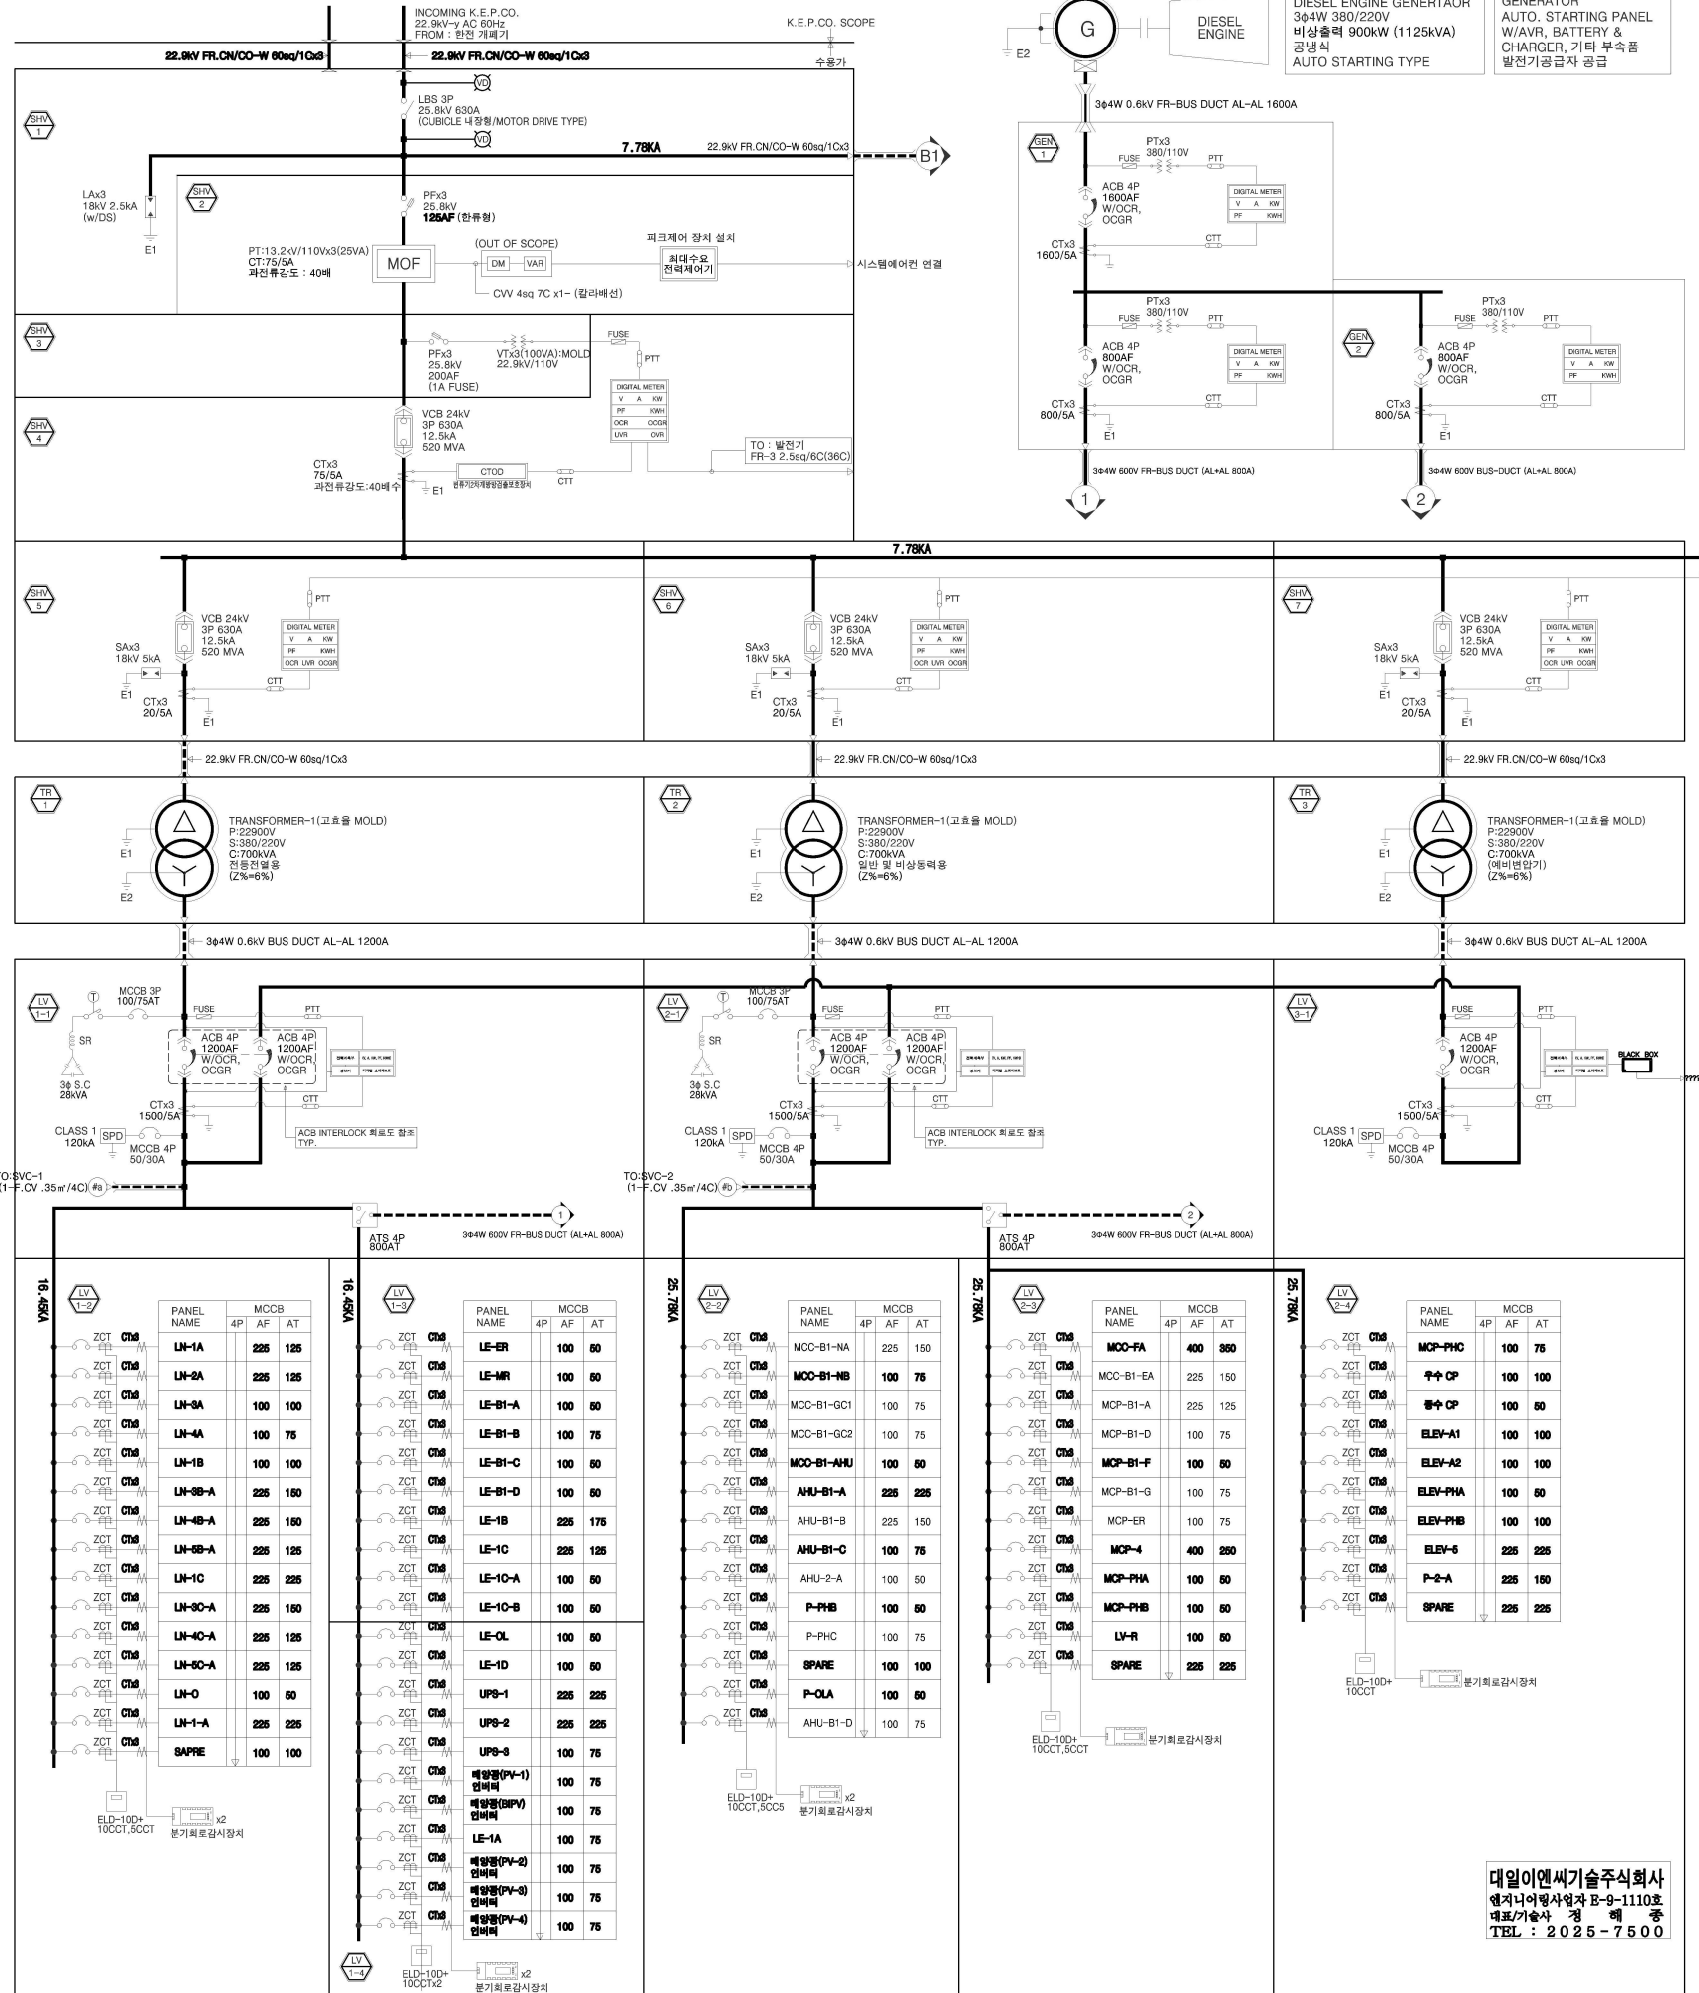

대일이엔씨기술주식회사
엔지니어링사업자 B-9-1110호
대표/기술사 정 해 중
TEL : 2025-7500

PROJECT TITLE

KE/CO

**한국전기안전공사
신사옥 건립 설계용역**

PRIME ARCHITECTS
heerim
HYUNDAI

STRUCTURAL CONSULTANT
[주]크로스구조연구소기술사사무소
TEL. 520-2835 FAX. 2057-2834

MECHANICAL CONSULTANT
엔지니어링엔 제트-9-535호
서울시 강남구 삼성동 40-9 삼성동 3-4호
TEL. 389-7221 FAX. 389-7226

ELECTRICAL CONSULTANT
대일 이엔씨 기술(주)
Dael Engineering & Consulting Co., Ltd.

FIRE PROTECTION ENGINEERS
(주)김영철이엔씨
서울시 강남구 가산동 470-8 K20빌딩 10층 1002호
대표번호 02-694-0110 팩스번호 02-694-0119

CIVIL CONSULTANT
SEKwang ENGINEERING CO., LTD.
(주) 세 광 엔 지 니 어 링
TEL. 567-2800 FAX. 565-1671

LANDSCAPE DESIGNER
그림+한

NOTE

* 에너지 절약 설계 기준

1. 변압기는 저손실형 변압기를 설치하였다.
2. 변압기별로 전력량계를 설치하였다.
3. 수전전압 25KV이하의 수전설비에 직접 강화 방식
4. 역률자동 코덴서를 집합설치할 경우 역률 자동조정장치를 채택
4. 전력사용량을 상시 감시하여 현재전력이 설정된 목표전력을 초과할 것이 예상될 경우 등특된 부하를 순차적으로 차단 및 투입. 최대수요전력을 목표값 이하로 관리 (SI 시스템과 연계하여 관리) - 최대 수요 전력제어 적용

↑ TO : 전력제어 서버 연결

분기회로감시장치 분기회로감시장치

분기회로감시장치 분기회로감시장치

A. 배전반에 사용할 MCCB는 단락전류를 계산 하여 다음과 같은 차단용량 이상을 사용한다. (LS기준 참고치며, 현장여건에 따라 변경가능)

TR	100F	225F	400F	600F	정격 차단 전류
TR-1	20kA	20kA	20kA	20kA	16.45kA 이상
TR-2	20kA	20kA	20kA	20kA	25.78kA 이상
TR-3	20kA	20kA	20kA	20kA	14.45kA 이상
TR-4	20kA	20kA	20kA	20kA	13.47kA 이상
TR-5	20kA	20kA	20kA	20kA	2.43kA 이상
TR-6	20kA	20kA	20kA	20kA	18.35kA 이상

REV **DATE** **DESCRIPTION** **DRN** **CHK** **APP**

DRAWING TITLE
수변전설비 단선 결선도-1

APPROVED 정영균, 김인기

CHECKED2 정해중, 강상태

CHECKED1 최병권, 김현민

DRAWN 이정수, 공준식

PROJECT NO. DB2011000201

SCALE A1 NONE A3 NONE

APPROVAL DATE 2012. 08.

DRAWING NO. E-02-01

REV. 0